
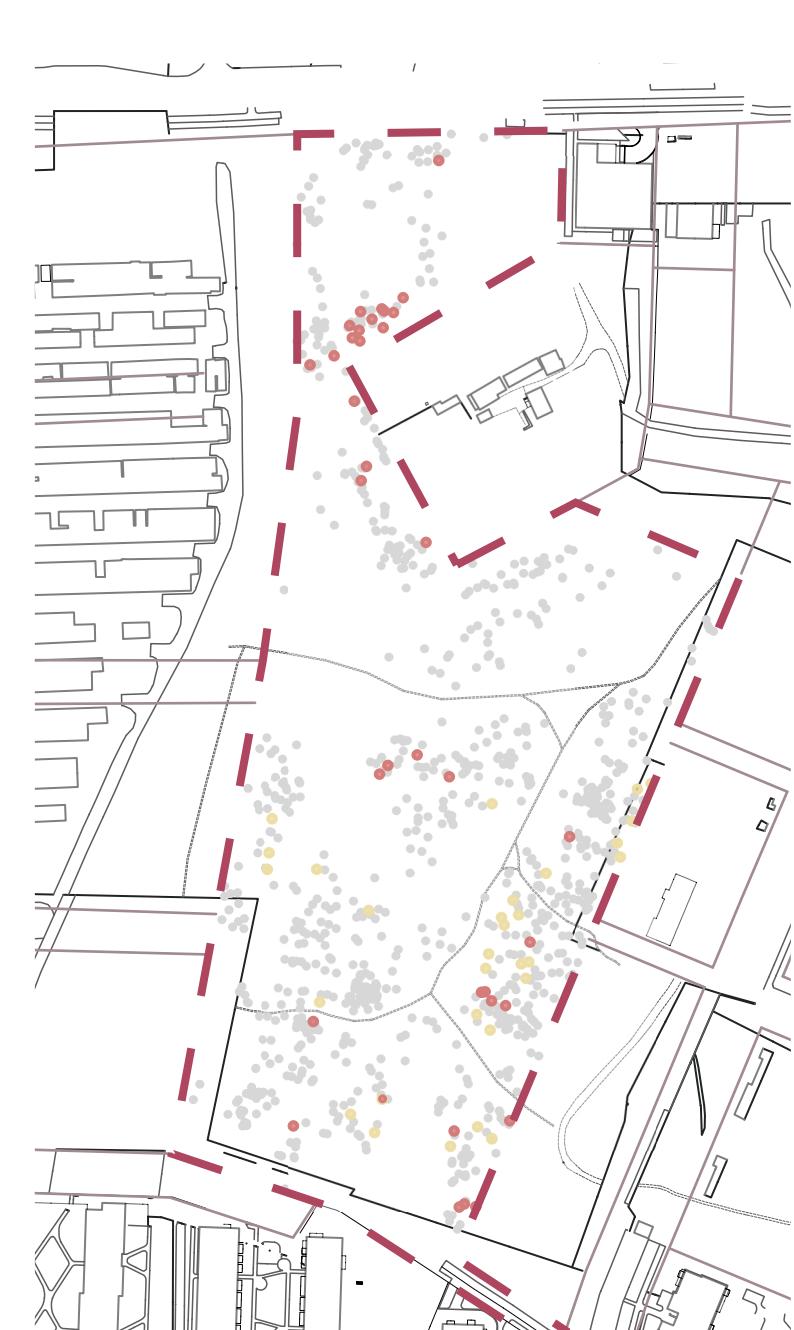
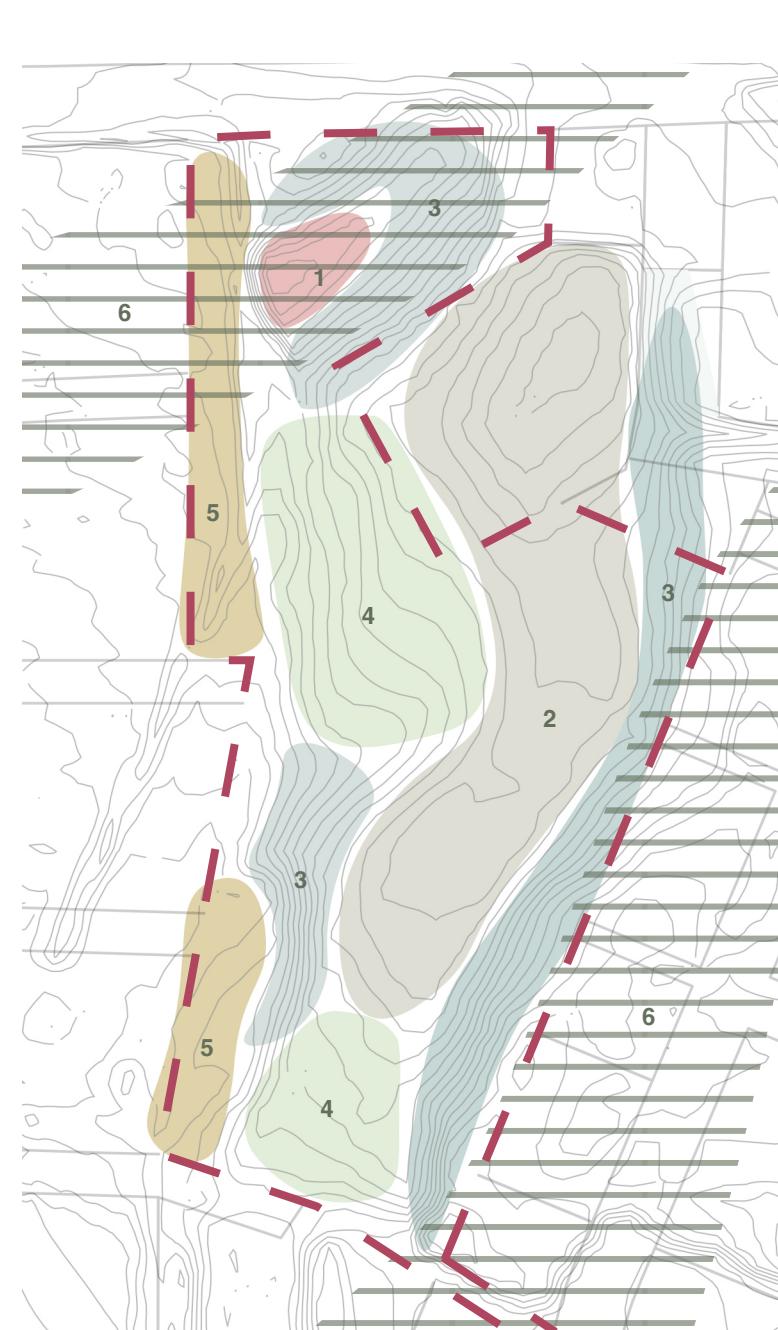
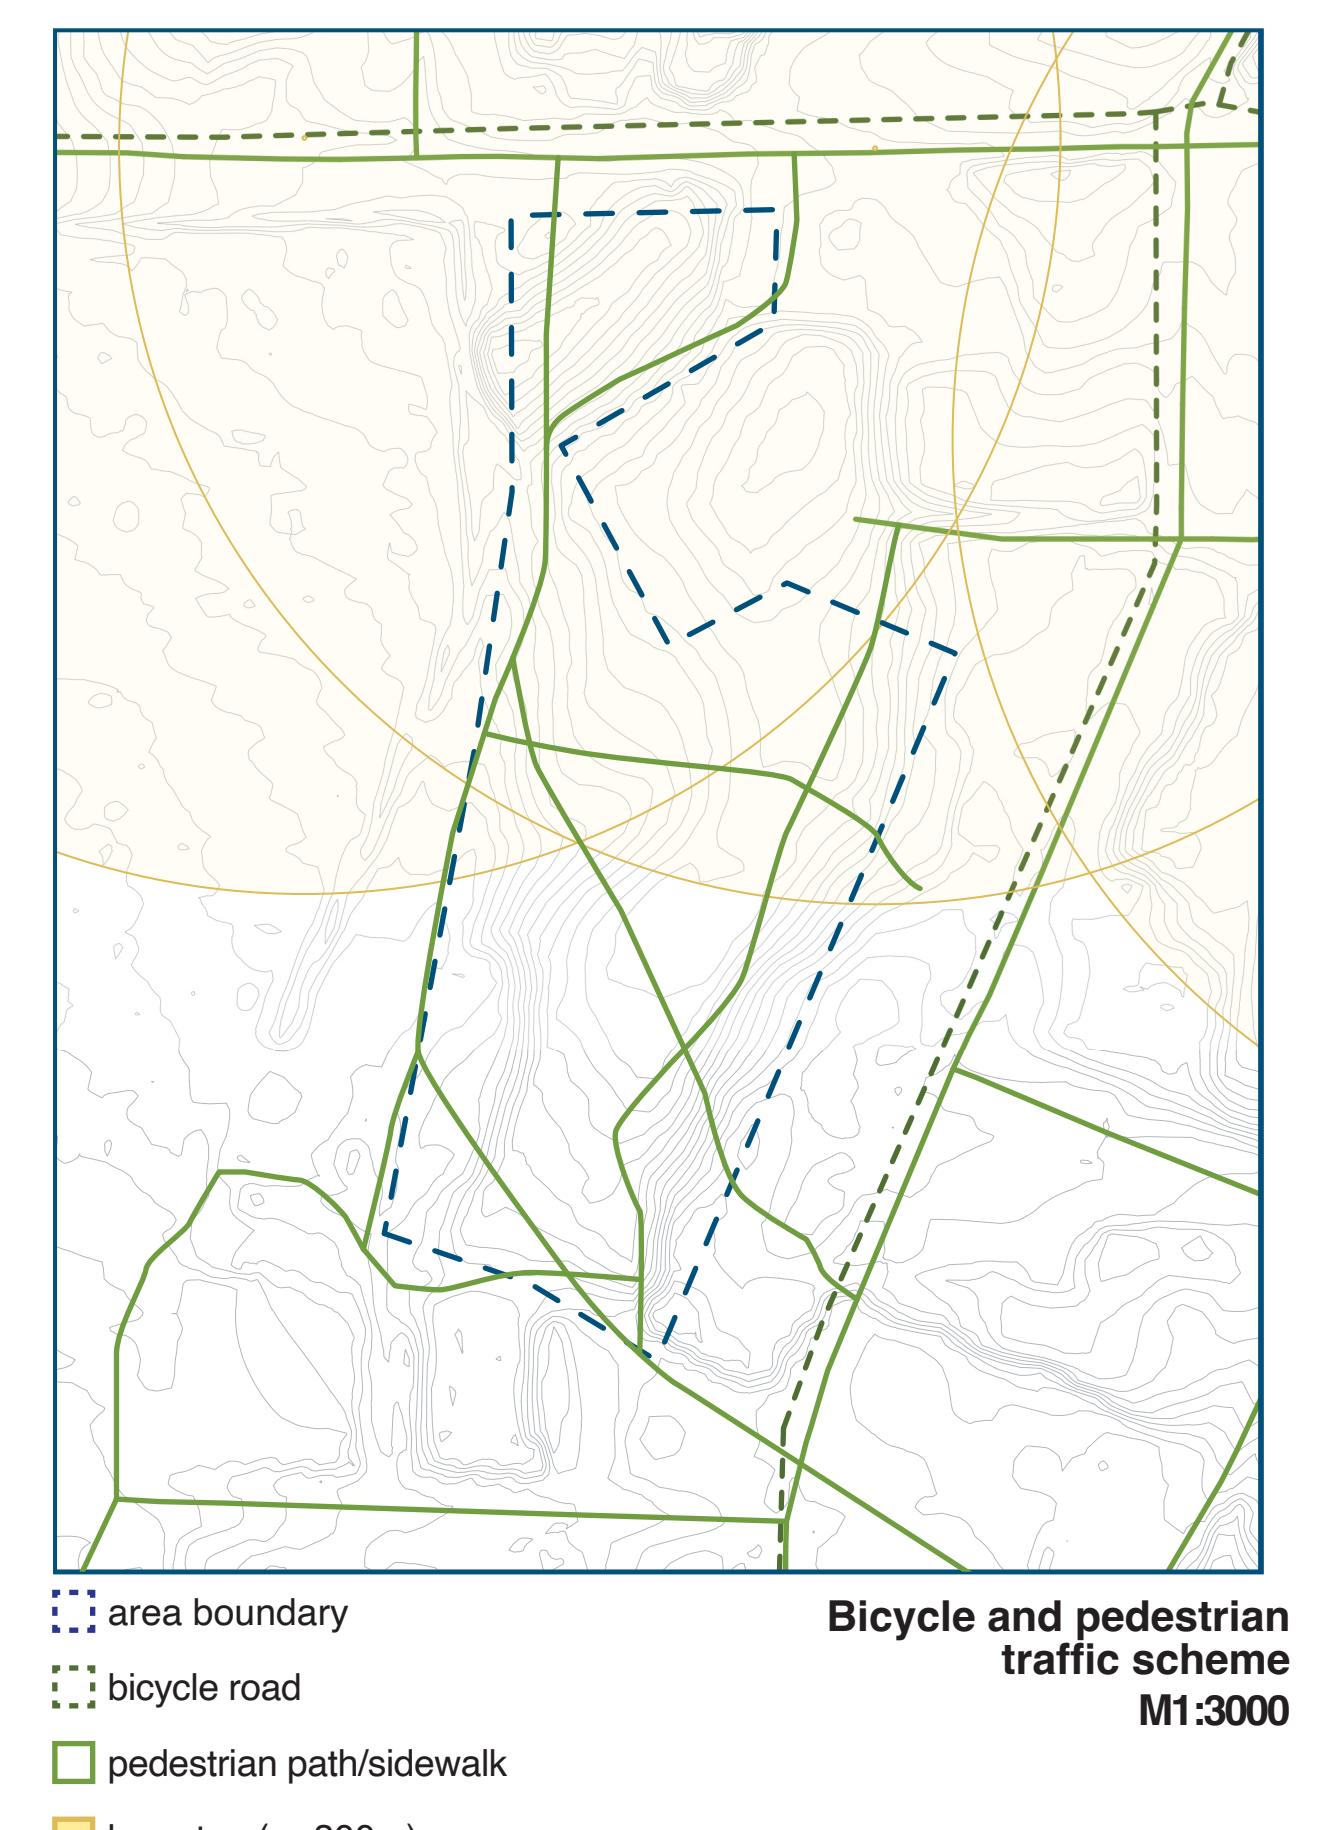
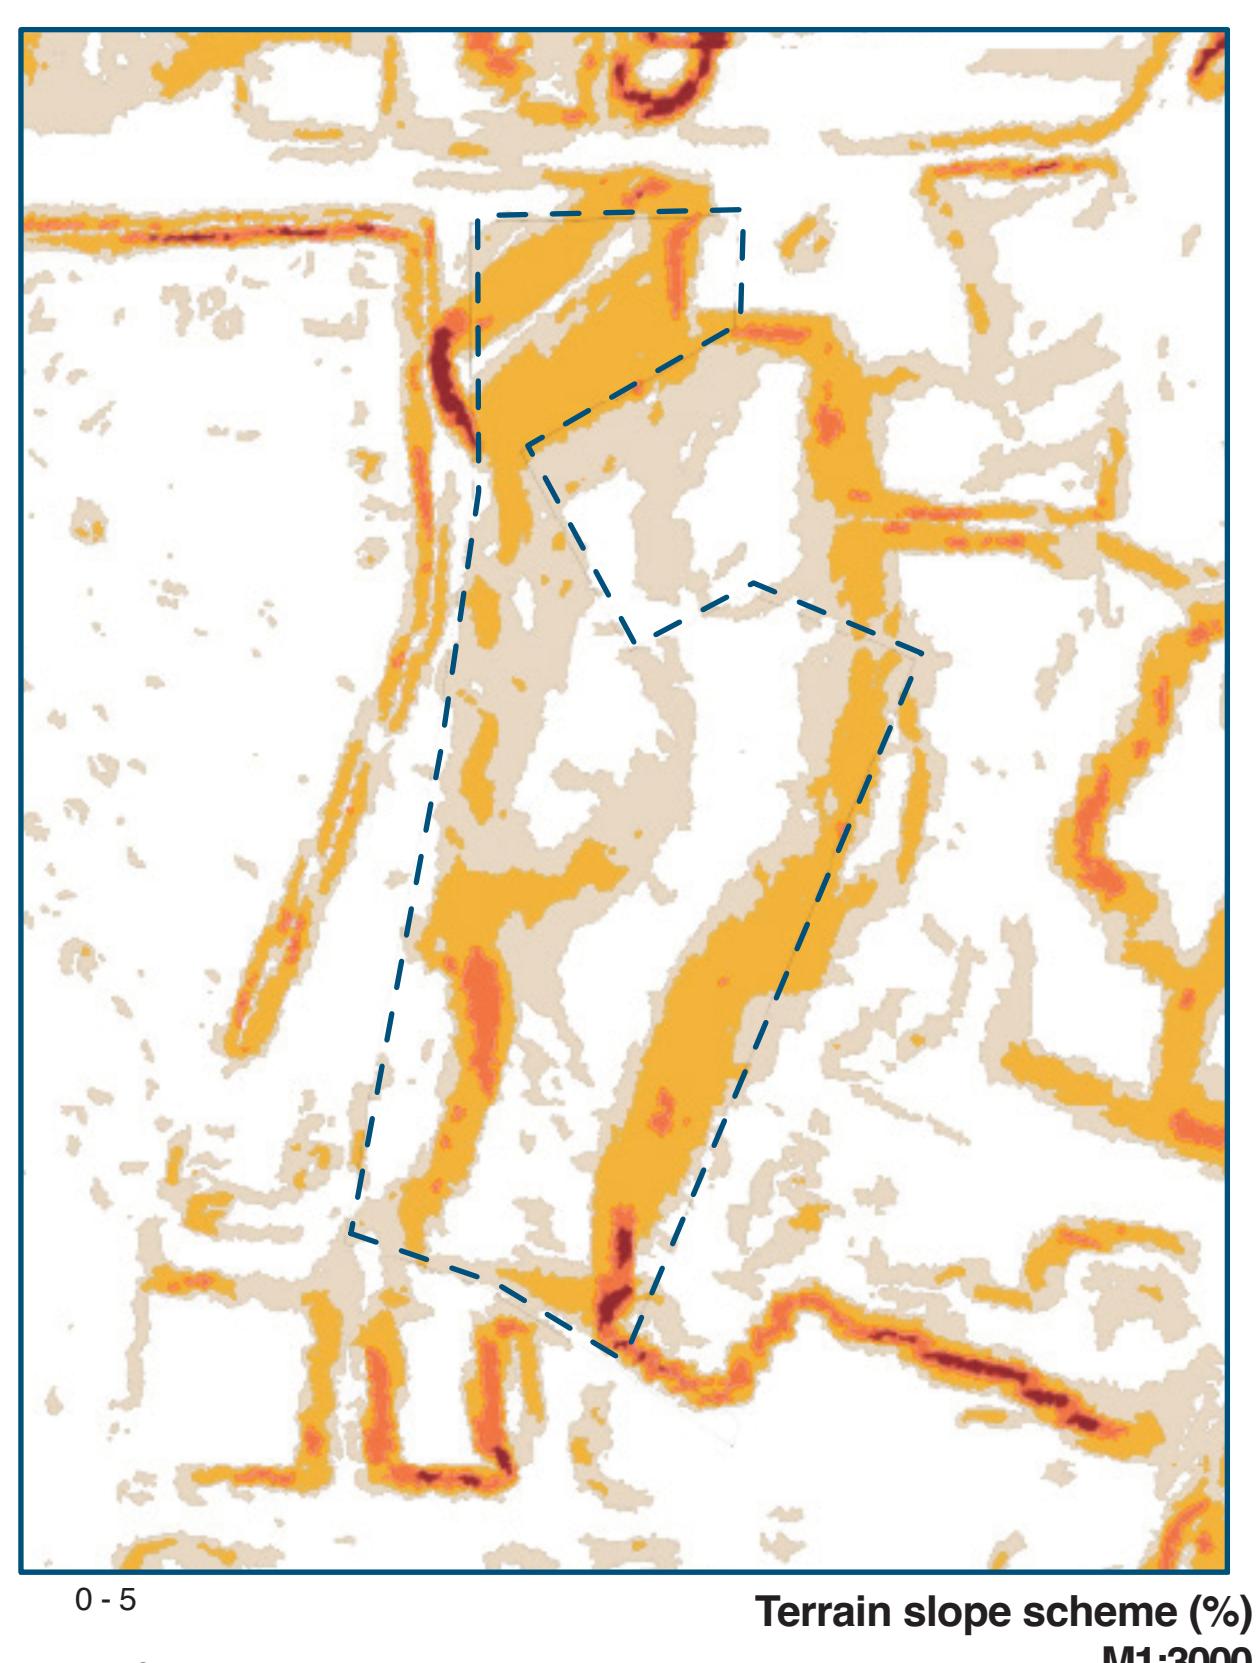
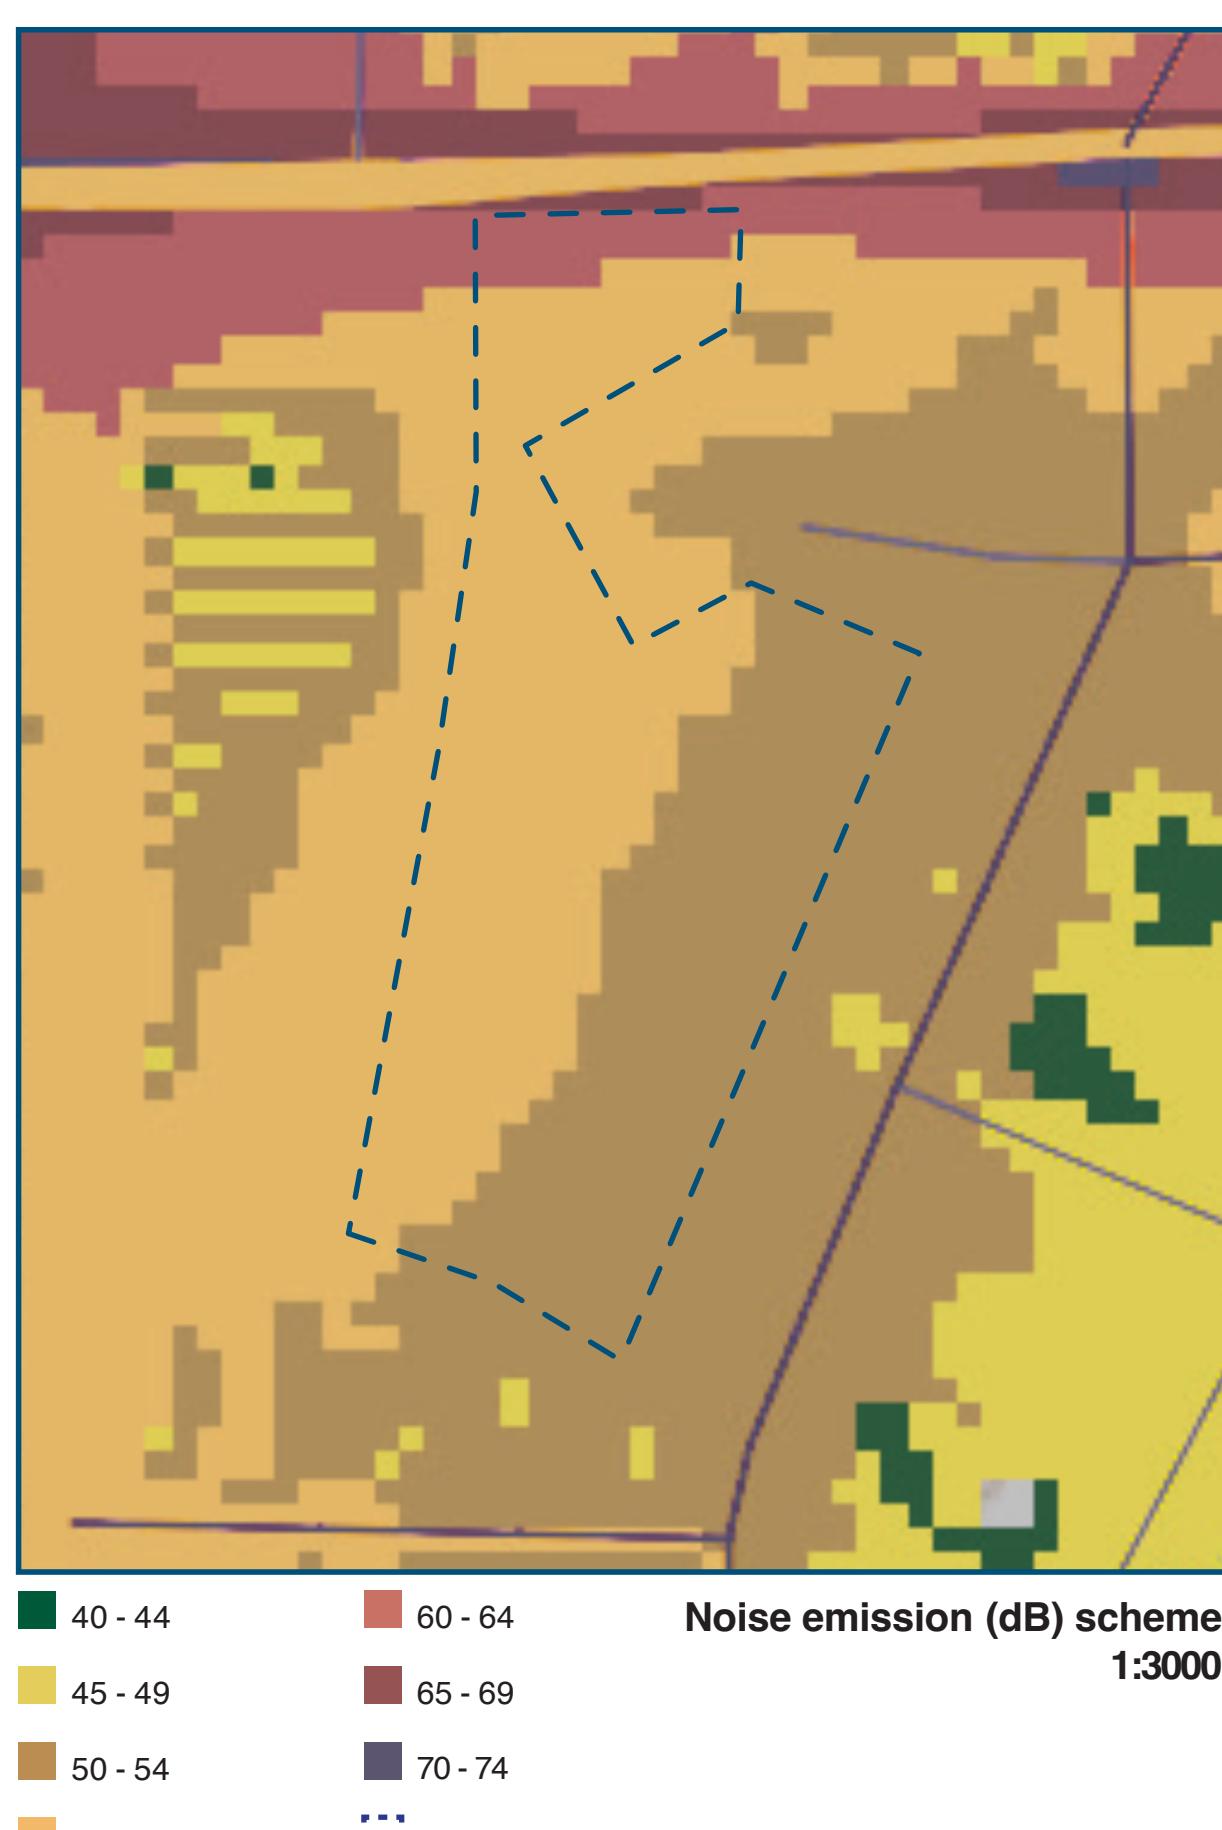


Terrain scheme
1:15000Function scheme
1:15000Footprint scheme
1:15000Traffic scheme (vehicle)
1:15000Traffic scheme (bicycle and
pedestrians)
1:15000

Landscape type unit (LTU) analysis 1:3000

LTU	Function	Landscape preservation	Forestation	Rainwater harvesting	Passive recreation	Active recreation	Gardening	Parking lots	Building
Dry valley Bottom (1)		●		○	○	○	○	○	○
Ridge top (2)		●	○	●	○	●	○	●	○
Slope (3)		●	●	●	●	●	○	○	○
Semi-flat slope (4)		○	●	●	●	●	●	●	●
Flat surfaces (5)		○	●	○	●	●	●	●	●
Dry valley (6)		○	○	●	○	○	○	○	○

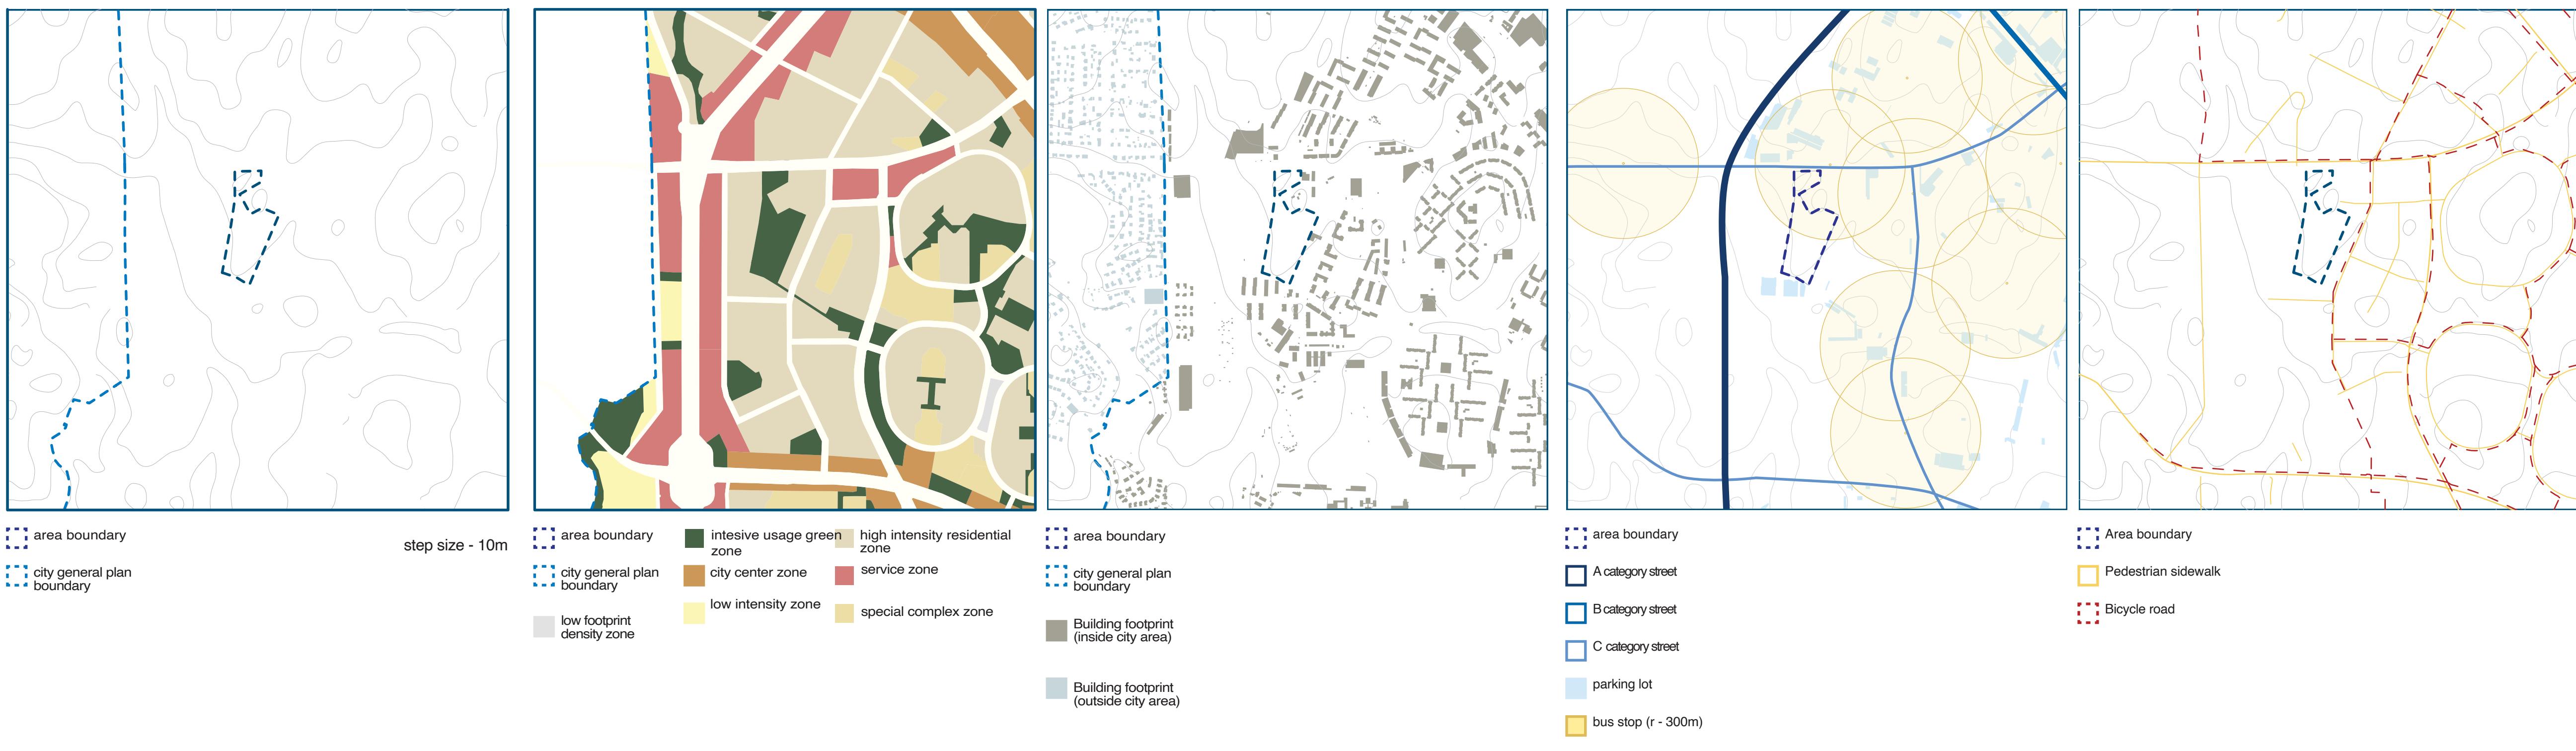